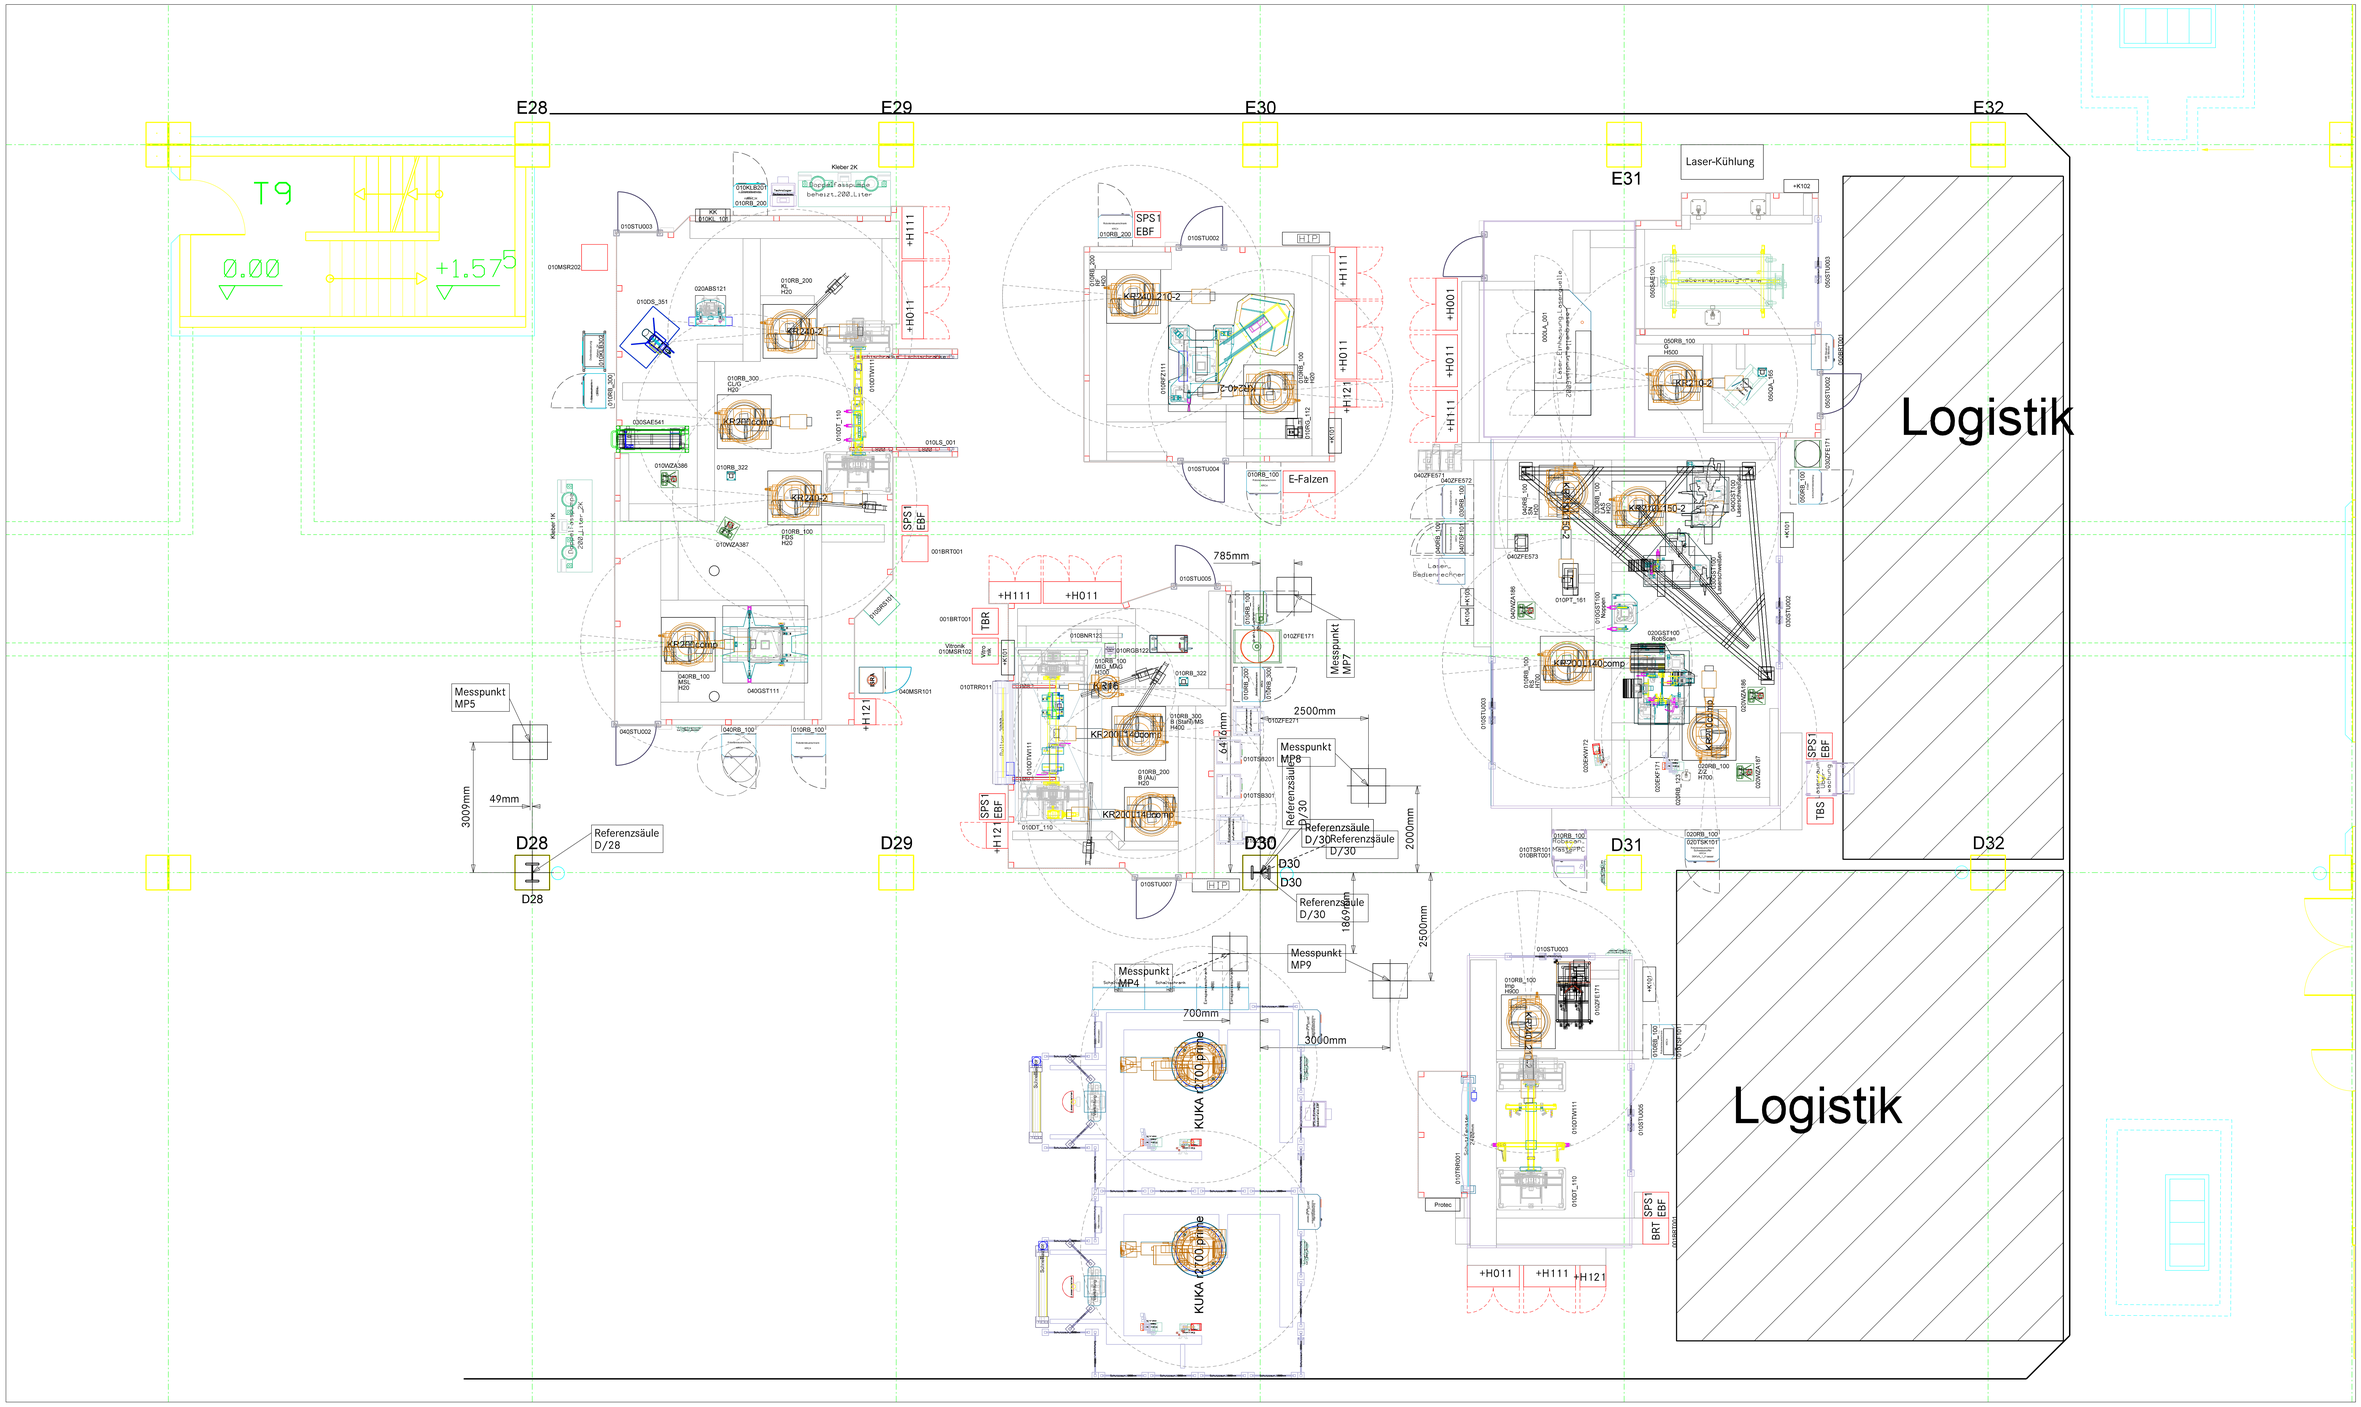

Zust.	Aenderung	Datum	Name
001	Ersterstellung		
002	Lieferstand 27.04.2012 Bezeichnung nach Walter geändert Layout entspricht Lieferung 002 vom 27.04.2012.	27.04.2012	EBZsjh

Projekt: MP04-09

Auftraggeber: DAIMLER AG

Planungsbüro: EBZ Ammerbuch GmbH

Kundenwerk: Werk Bremen (W67)

Issue/: | Year: | Type: | original:

Blatt-Nr.: 1

Gesamtlayout DAG BR205
Master Pieces 04-09

Erst. 30.11.2011 | Bearb. S.Maier | Gepr. | Norm.

Maßstab: 1:50

F1 - 6500000XXXX00000000BR205