Zust.	Aenderung	Datum	Name
001	Ersterstellung		
002	Lieferstand 27.04.2012: Bezeichnung nach Ruplan geändert Layout entspricht Lieferung 002 vom 27.04.2012.	27.04.2012	EBZ/ph

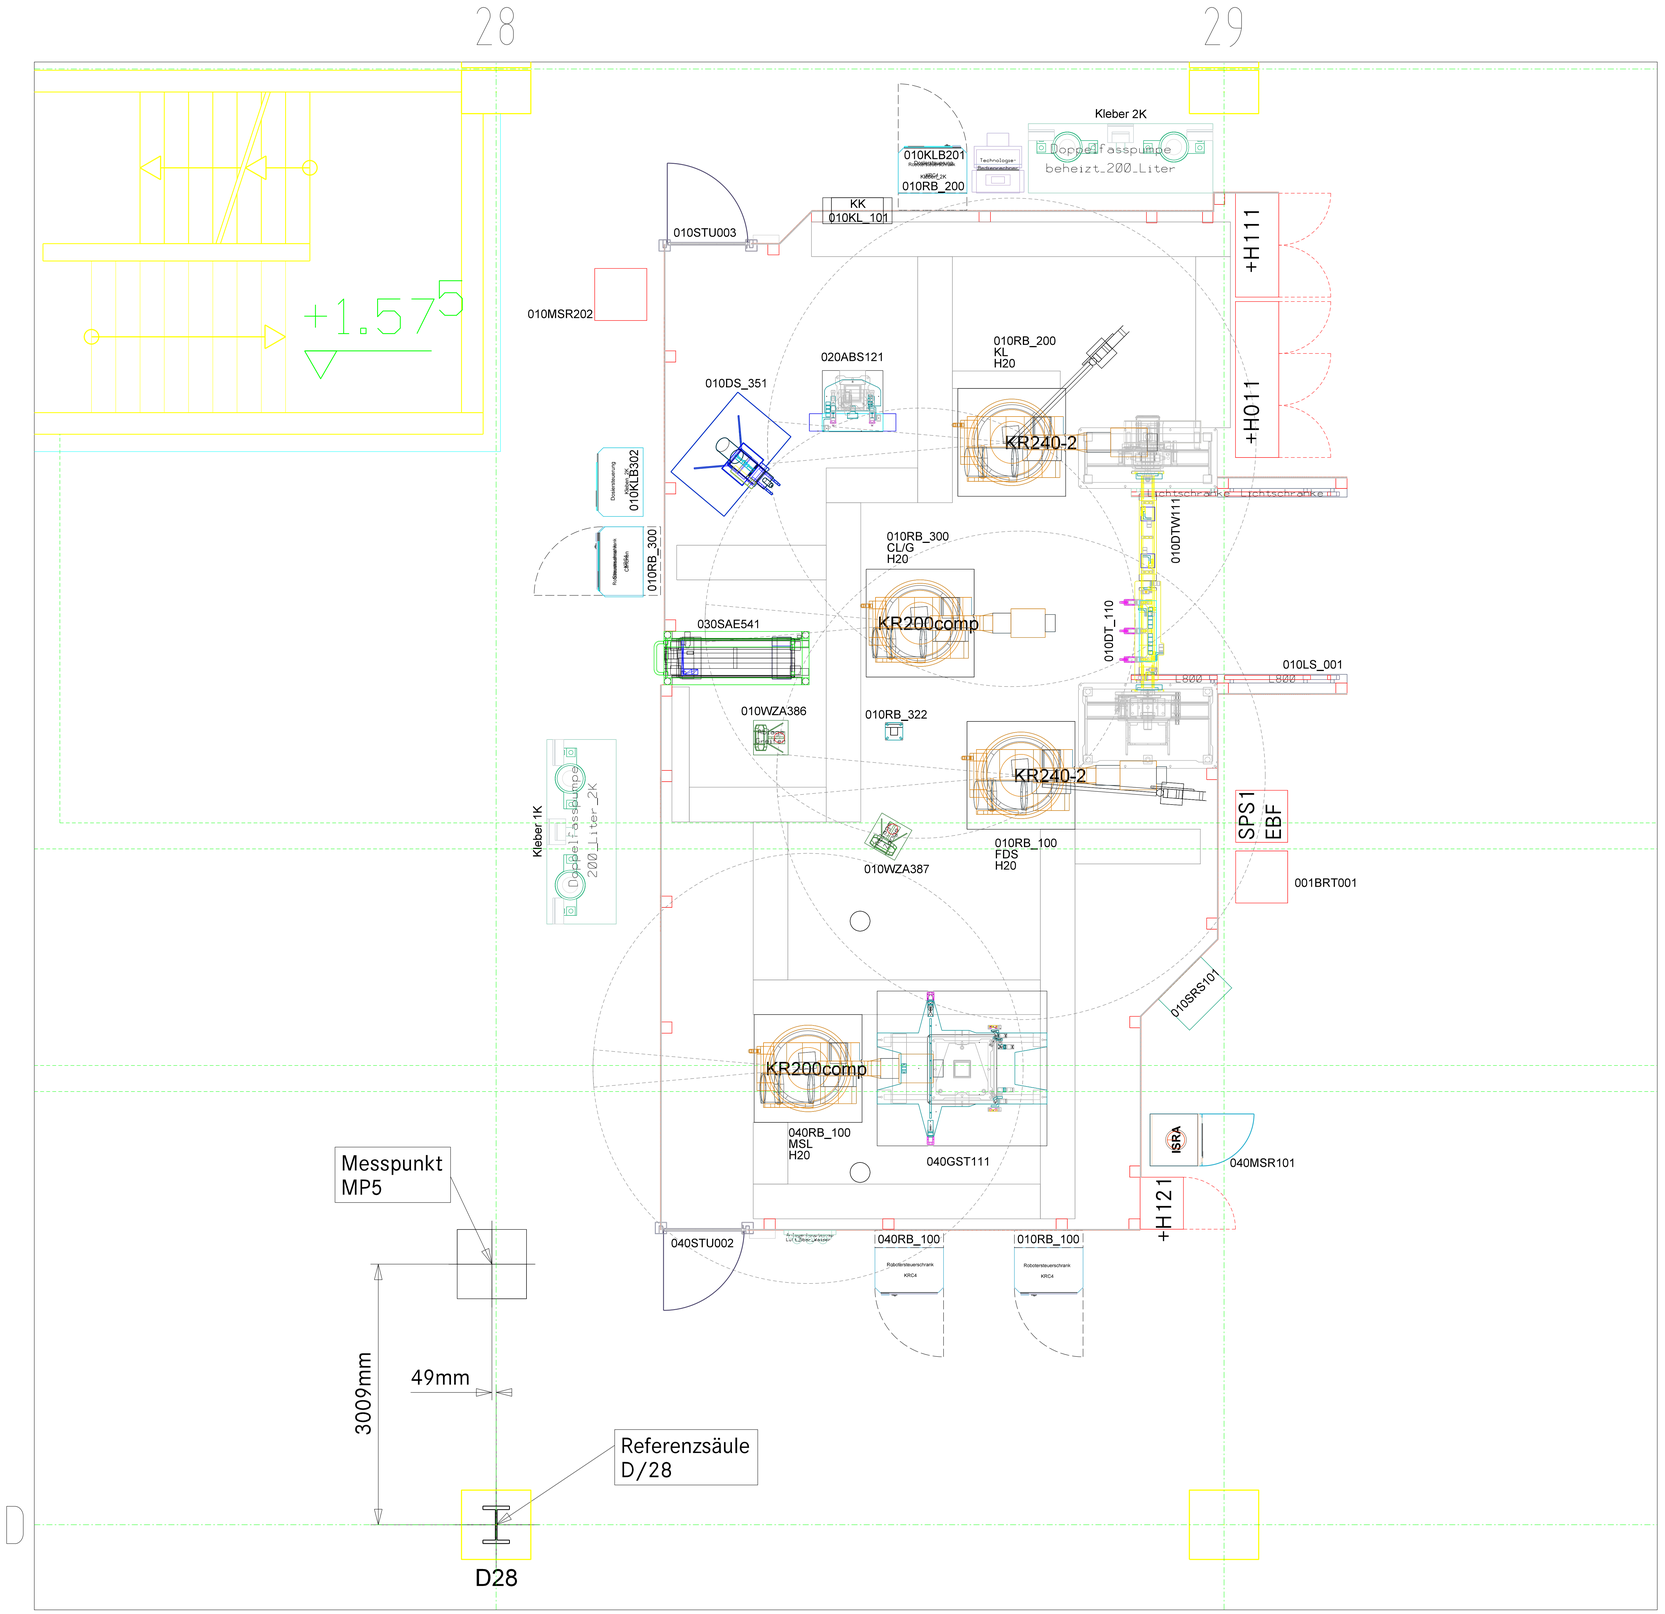

Projekt: MP05

aufgegeben: DAIMLER AG

EBZ Ammerbuch GmbH

Projektnummer: Werk Bremen (W67)

Stand: -
Sach: -
Typ: -
aufgenl: -

Variante:
Blatanz.:
Blatt: 1

Layout DAG BR205
Master Pieces 05

Datum: 06.02.2012 Bearb.: L.Maier
Gepr.: Norm:
Maßstab: 1:25

F1 - 650000011470000000000BR205