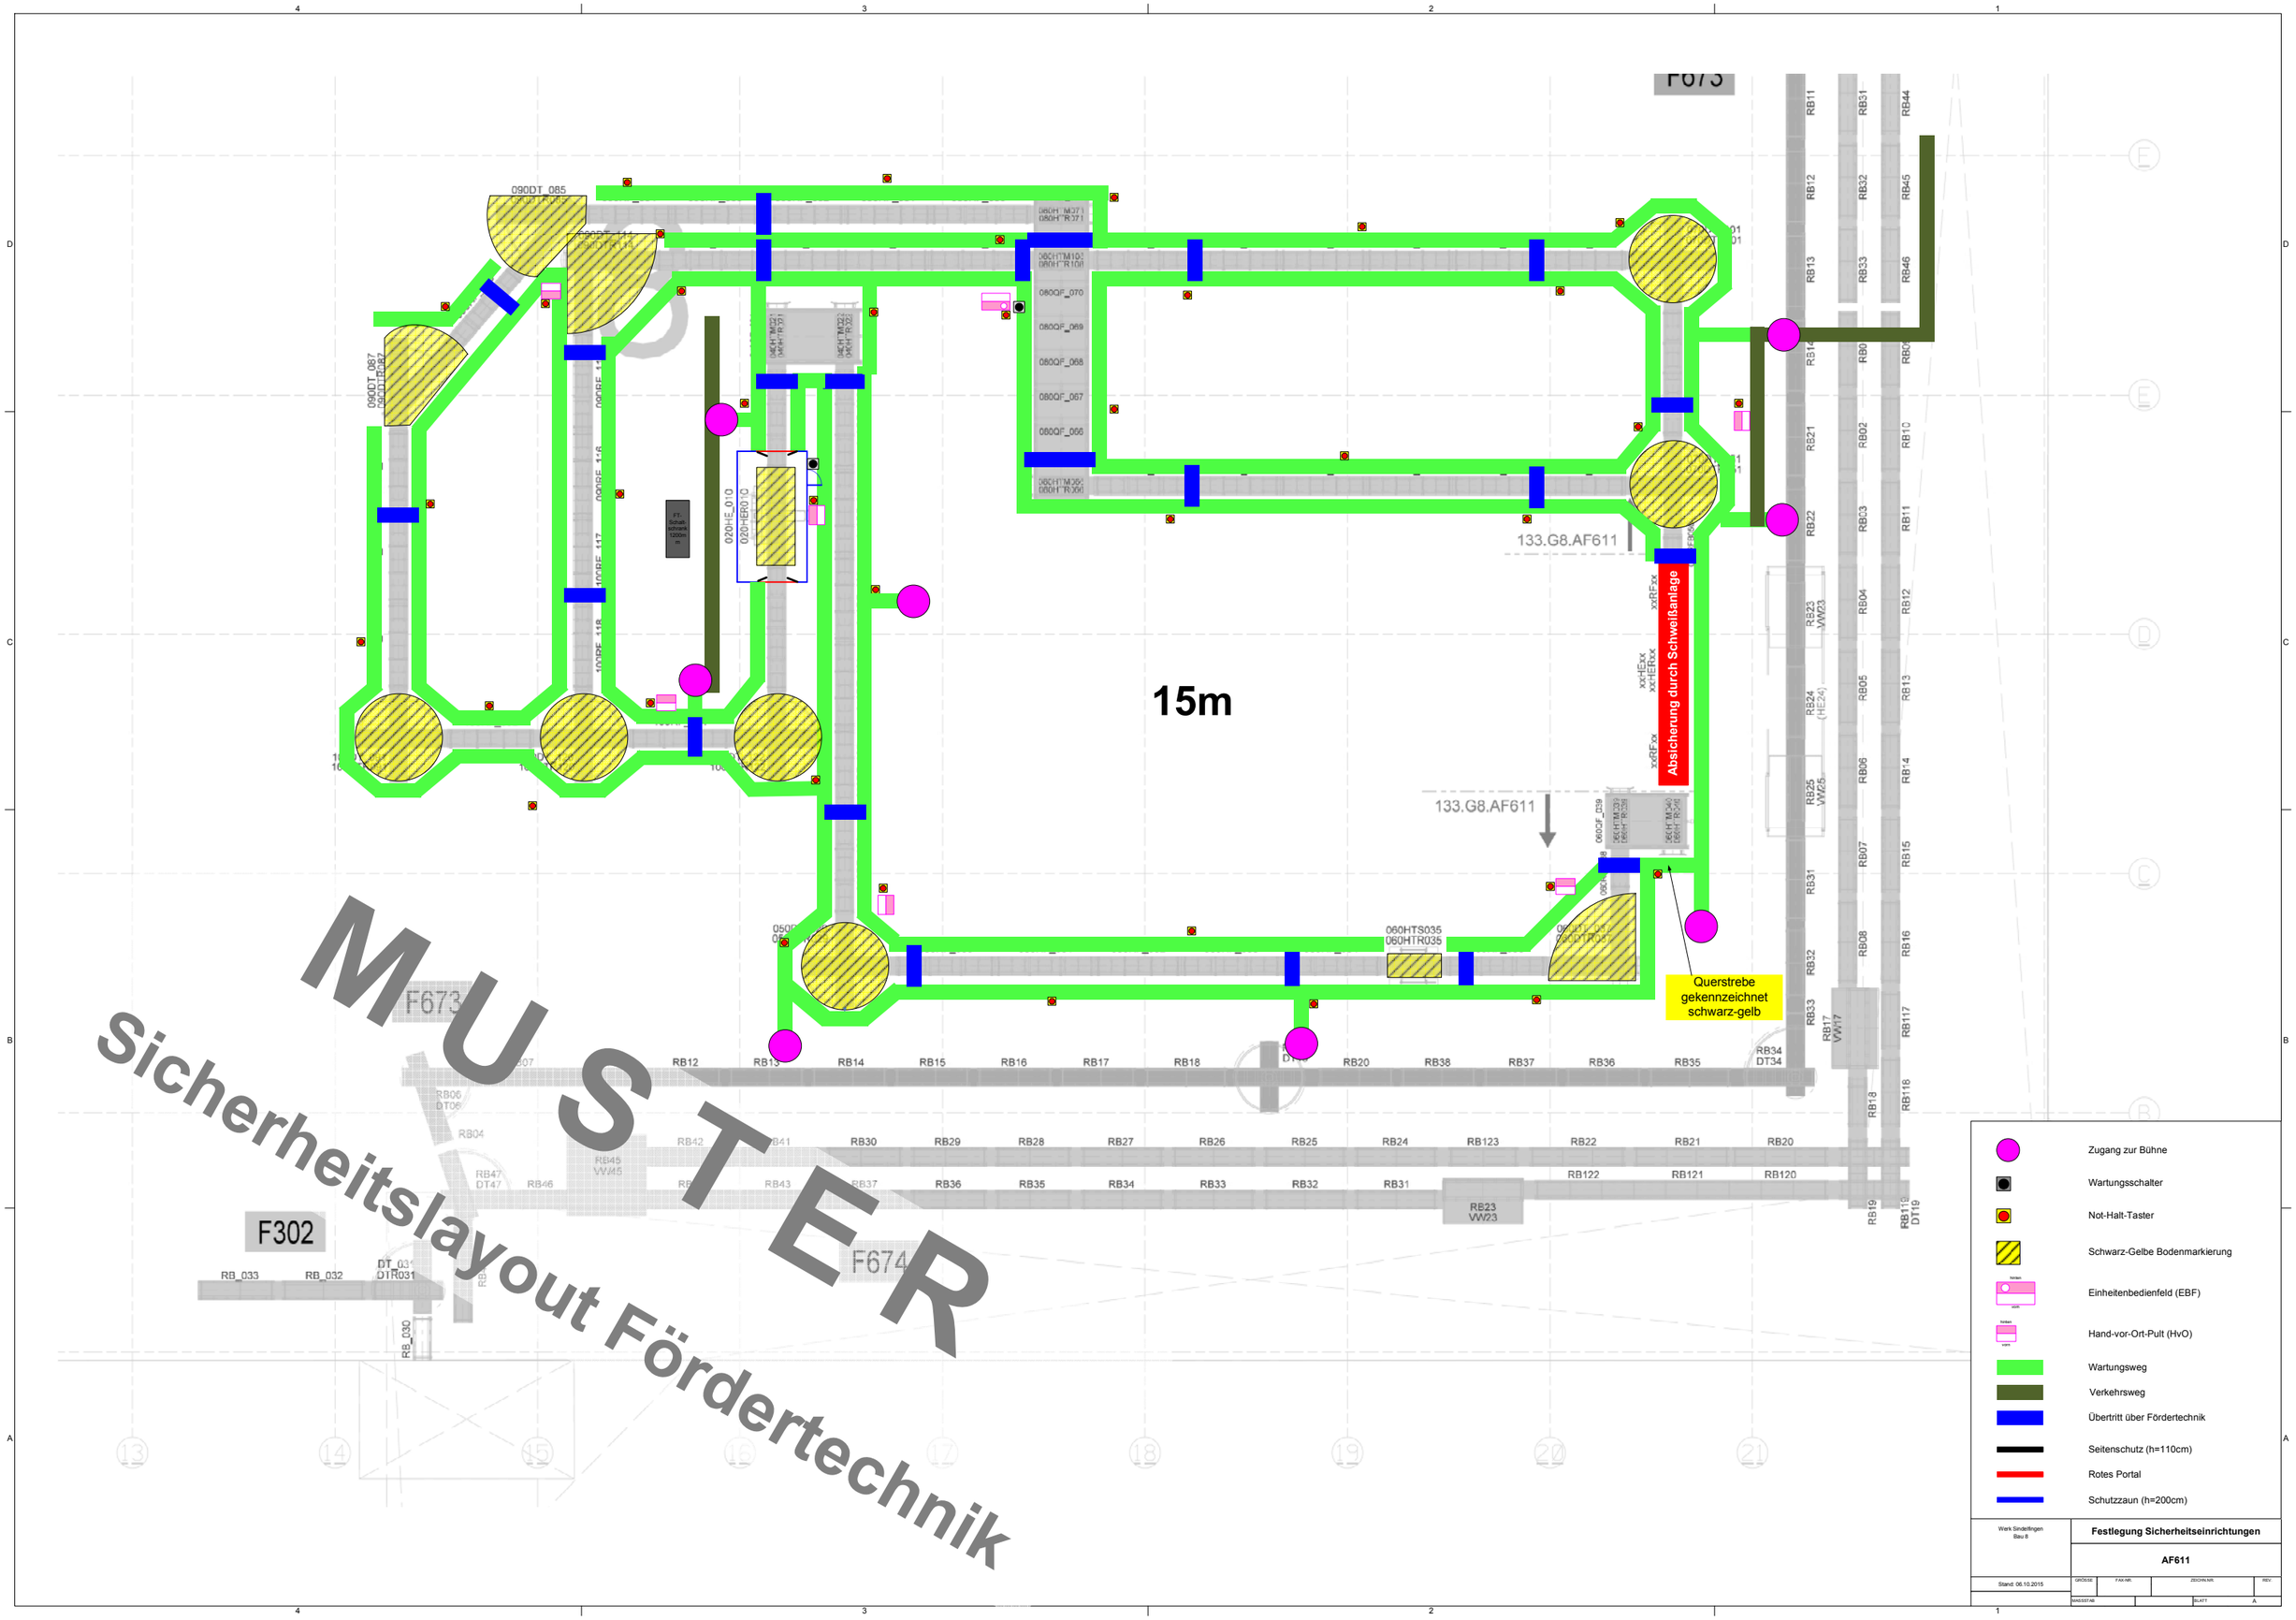
F673
F674
F302
15m
133.G8.AF611
Absicherung durch Schweißanlage
Querstrebe gekennzeichnet schwarz-gelb
060HTS035
060HTR035
090DT_085
090DT_087
020HE_010
MUSTER
Sicherheitslayout Fördertechnik
Zugang zur Bühne
Wartungsschalter
Not-Halt-Taster
Schwarz-Gelbe Bodenmarkierung
Einheitenbedienfeld (EBF)
Hand-vor-Ort-Pult (HvO)
Wartungsweg
Verkehrsweg
Übertritt über Fördertechnik
Seitenschutz (h=110cm)
Rotes Portal
Schutzzaun (h=200cm)
Werk Sindelfingen
Bau 8
Festlegung Sicherheitseinrichtungen
AF611
Stand: 06.10.2015

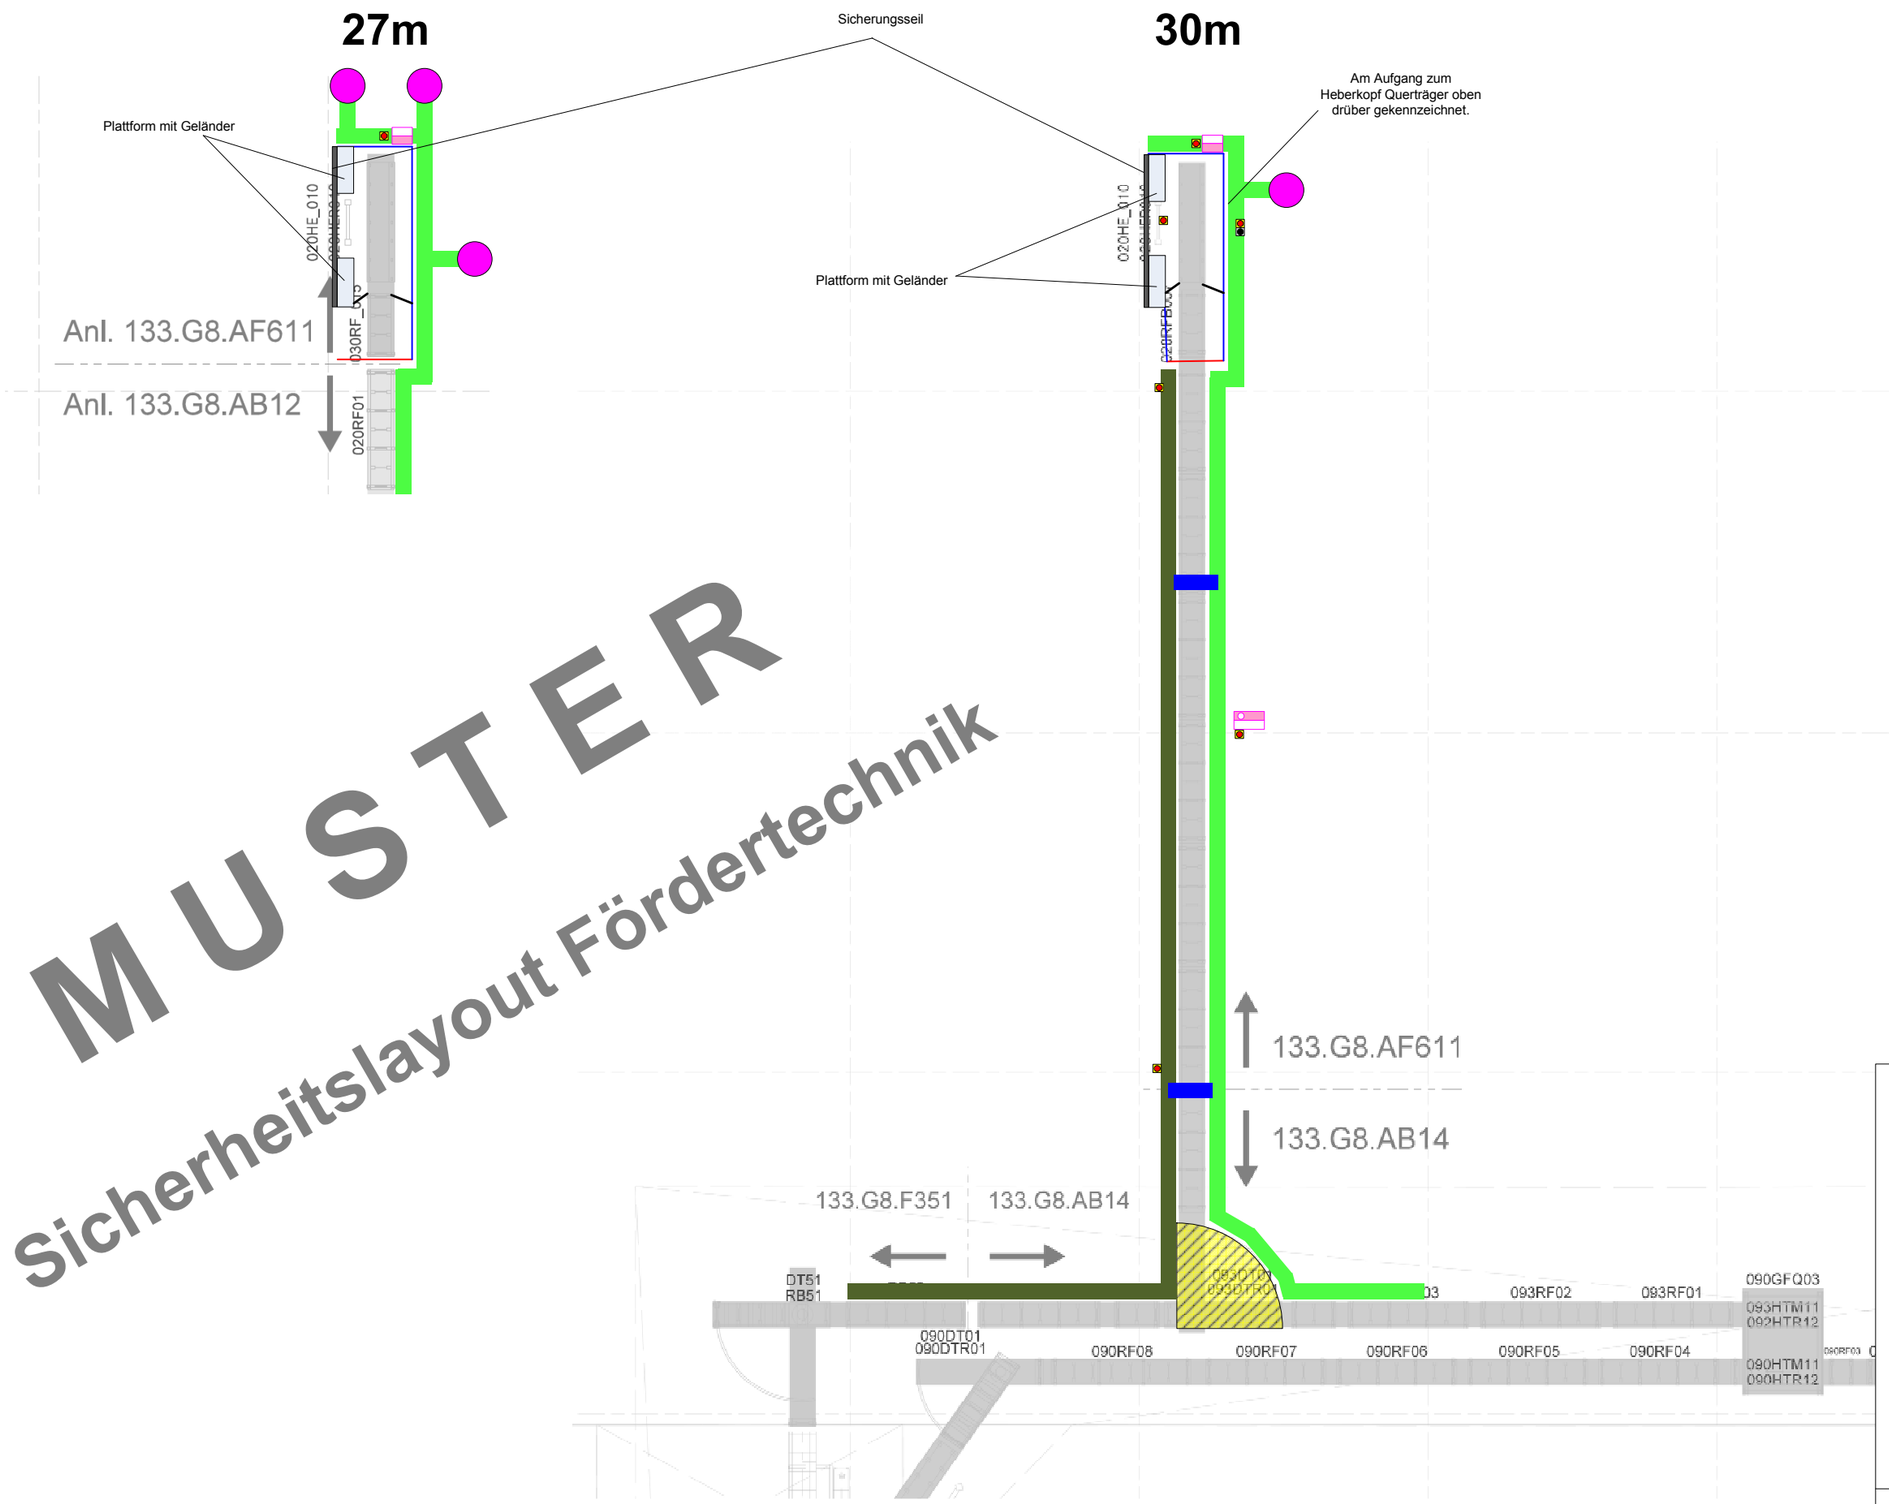

Zugang zur Bühne
Wartungsschalter
Not-Halt-Taster
Schwarz-Gelbe Bodenmarkierung
Einheitenbedienfeld (EBF)
Hand-vor-Ort-Pult (HvO)
Wartungsweg
Verkehrsweg
Übertritt über Fördertechnik
Seitenschutz (h=110cm)
Rotes Portal
Schutzzaun (h=200cm)

MUSTER
Sicherheitslayout Fördertechnik

Werk Sindelfingen
Bau 8

Festlegung Sicherheitseinrichtungen

AF611, AB14

Stand: 06.10.2015

GROSSE	FAX-NR.	ZEICHN.NR.	REV.
MASSSTAB		BLATT	A